QIDDIYA DEVELOPMENT COMPANY

DOCUMENT NUMBER:	QDC-ADM-TEM-QMS-00007	REVISION NUMBER:	0D	ISSUED BY:	PMO
DOCUMENT TITLE	MIR FORM	DOCUMENT TYPE:	FORM	DATE ISSUED:	MAY-08-2022

MATERIAL INSPECTION REQUEST (MIR) FORM

Contractor:	HAIF COMPANY
Project:	QPMO-410-CT-00618- ROAD ACCESS TO RESORT CORE
Contract No.:	QI09043311-VO-0004
Material Inspection Request Number:	QRXM114000-HFC-TEC-MIR-ITS-02-RO5-00016

HAIF-FREYSSINET JV

Discipline

Architecture	☐	Mechanical	☐	Information Technology	☐	Quality	☐	Project Controls	☐
Civil/Structural	☑	Electrical	☐	Landscape	☐	Safety	☐	Construction Management	☐
Other	☐								

MATERIAL DESCRIPTION

Inspection / Test Location:	INTERIM ROAD MAIN LINE-02		
Material Name:	ITS SYSTEMS (TRAFFIC SIGNALS POLE W / TOP BOLTED)	Quantity:	31 Nos.
P.O Number		Delivery Note Number:	TTSDN-HAIF-060726-026
Approved Material Transmittal Number: (Aconex document Approval)	QRXM114000-HFC-TEC-MAT-ITS-02-RO5-00015	Approval Date:	
Inspection Date:	02-Aug-2026	Inspection Start Time:	10:00 AM
ITP:	QRXM114000-HFC-TEC-ITP-ITS-02-RO5-00006	Checklist:	HFC-CKL-9001
Spec's / Dwg. Ref.:	TRAFFIC TECH SECURITY W.L.L	Approved Method Statement Number:	
Attachments:	Test Certificate: ◉ Yes ○ No		
	IFC / Shop Drawings: ○ Yes ◉ No		

DESCRITPTION OF MATERIAL

Traffic Signal Pole 3.7 Mtrs (31 Nos.) 3.7 Tublar Traffic Signal Pole W/ Top Bolted Cap & Base PlateOnly. DWG. No. S-9571. Rev.-02 (31Nos.) Powder Coating Charges For The 3.7 m Pole (31 Pcs.) for Interim Road Main Line-02

CONTRACTOR - QUALITY INSPECTOR - INITIAL INSPECTION FINDINGS:

Are Complete Details Mentioned in P.O and Delivery Note?	◉ YES ○ NO	REMARKS	
Complies with Approved ITPs/Checklists?	◉ YES ○ NO	REMARKS	
Signs of Physcial Damage?	○ YES ◉ NO	REMARKS	
Conforms to Approved Material Submittal?	○ YES ○ NO	REMARKS	

Accepted:	◉
Accepted with Comments:	○
Rejected (See Remarks):	○

REMARKS:					
Name:	Moataz Elkhateeb	Signature:		Date:	02-08-2026

QIDDIYA / SUPERVISION CONSULTANT QC INSPECTOR - FINAL INSPECTION FINDINGS:

Contractor Has complied with Material requirements?	○ YES ○ NO	Materials Are Stored correctly?	○ YES ○ NO ○ NA

Accepted:	○
Accepted with Comments:	◉
Rejected (See Remarks):	○

REMARKS:	Inspection done For delivered material in the site Store area and Found as per delivery note & matched approval				
Name:	Abdelrahman Hassan	Signature:		Date	2/8/2026

FOR DETAILED MATERIAL INSPECTION STATUS, PLEASE SEE ATTACHED CHECKLIST.
CHECKLISTS THAT ARE NOT ATTACHED AND SIGNED BY SUPERVISION CONSULTANT WILL VOID THIS INSPECTION REQUEST.

This document is the property of Qiddiya Development Company, 2022

*Final approval subject to provide MTC for Traffic pole Post.
* provide welding certificate.

Client:	Consultant:	Contractor:
Qiddiya	Zuhair Fayez Partnership	Hail Company / Freyssinet — HAIF-FREYSSINET JV

TECHNICAL DOCUMENTS

Project Name: Package 3 - **Interim Road Access to Resort Core**	**Project Code:** QRXM114000
Location: 00	**Date:** 15-November-2025
Document Title:**Material Approval Request FOR ITS SYSTEM SUPPLYING & INSTALLING BY TRAFFIC TECH SECURITY W.L.L** (Traffic Signal Poles and Gantries)	**Ref No:** QRXM114000-HFC-TEC-MAT-ITS-02-RO5-00015
	Rev No: 00

Department: ☐ Architectural ☐ Structural ☐ Electrical ☐ Mechanical ☑ ITS ☐ Civil

Type: ☐ Pre-Qualification ☐ Method Statement ☒ Material Submittal ☐ Sample ☐ Other

Document Description:Material Approval Request FOR ITS SYSTEM SUPPLYING & INSTALLING BY TRAFFIC TECH SECURITY W.L.L (Traffic Signal Poles and Gantries)

Doc. Ref. No.	Title
QRXM114000-HFC-TEC-MAT-ITS-02-RO5-00015	**Material Approval Request FOR ITS SYSTEM SUPPLYING & INSTALLING BY TRAFFIC TECH SECURITY W.L.L** (Traffic Signal Poles and Gantries)

Enclosure:

Submitted By:	**Received By:**
Name: **Eng. Moataz** Signature: Date:15-Nov-2025	Name: Signature:

Below portion for Consultant Supervision use only

Status: ☐A- Approved ☐B- Approved as noted ☐C- Revise & Resubmit ☐R- For information only

Comments:

B: Approved with Comments
Saud Nawab
Zuhair Fayez Partnership Consultants
Riyadh , Saudi Arabia

1- Technical comparison sheet must be stamped by Contractor/Supplier.
2- Height of poles & length of gantries shall be as per approved shop drawings.
3- Weather proof non- degradable heat resistant rubber shall be provided for all access doors
4- Contractor shall ensure that all poles and gantries are compatible with the mounted devices such as Vehicular and Pedestrian Signal Heads, Push Buttons, LPR Cameras, EVP, TSP, and VDS units etc.
5- Poles and gantries specification shall be as per pole manufacturer's recommendations.
6- Galvanization & Compliance Certificates to be provided at stage of MIR
7- Provide SASO certificate for proposed material.
8- All the material shall be in compliance with project specification and relevant standards.

B: Approved with Comments
Saud Nawab
Zuhair Fayez Partnership Consultants
Riyadh , Saudi Arabia

B: Approved with Comments
Zuhair Fayez Partnership Consultants
Riyadh , Saudi Arabia

Below portion for Client use only

Comments:

Signed by: Signature: Date:

Client:	Consultant:	Contractor:
Qiddiya	Zuhair Fayez Partnership	Haif Company HAIF-FREYSSINET JV

TECHNICAL DOCUMENTS

Project Name: Package 3 - Interim Road Access to Resort Core	**Project Code:** QRXM114000
Location: 00	**Date:** 4 -June-2026
Document Title: **Inspection & Test Plan for Inteligent Transportation System Works for TRAFFIC SIGNAL SYSTEM**	**Ref No:** QRXM114000-HFC-TEC-ITP-ITS-00006
	Rev No: 00

Department: ☐ Architectural ☐ Structural ☒ Electrical ☐ Mechanical ☐ Authority ☐ Civil

Type: ☐ Pre-Qualification ☐ Method Statement ☐ Material Submittal ☐ Sample ☒ ITP

Document Description: This is Inspection&Test Plan for Inspection&Test Plan for Inteligent Transportation system Works for TRAFFIC SIGNAL SYSTEM

Doc. Ref. No.	Title
QRXM114000-HFC-TEC-ITP-ITS-00005	**Inspection&Test Plan for Inteligent Transportation system Works for TRAFFIC SIGNAL SYSTEM**

Enclosure:

Submitted By:	**Received By:**
Name: Eng. Moataz Signature: Date: 4 -June-2026	Name: Signature: Date:

Below portion for Consultant Supervision use only

Status: ☐A- Approved ☐B- Approved as noted ☐C- Revise & Resubmit ☐R- For information only

Comments: All the work shall be carried out inaccordance with project specification, relevant standards & codes and manufacturer recommendations.

A: Approved
Zuhair Fayez Partnership Consultants
Riyadh , Saudi Arabia

A: Approved
Saud Nawab
Zuhair Fayez Partnership Consultants
Riyadh , Saudi Arabia

A: Approved
Zuhair Fayez Partnership Consultants
Riyadh , Saudi Arabia

Below portion for Client use only

Comments:

Signed by: Signature: Date:

HAIF-FSA JV Inspection & Test Plan					I &TP	APPROVED DATE	DISCIPLINE ITS	
Inteligent Transportation Sytem Works for TRAFFIC SIGNAL SYSTEM					**HFC-ITP-090**			
PROJECT TITLE/WBS Awes Road To Nasser Cornish (RA2RC)					CONTRACTOR/SUBCONTRACTOR			
WIR No.					CONSTRUCTION- Intelligent Transportation System Works for TRAFFIC SIGNAL SYSTEM		HAIF	

ITEM NO.	PROJECT PHASE	TASK / ACTIVITY	Quality Requirements /references/ specifications	Quality Record	INSPECTION RESPONSIBILITY ASSIGNMENTS			REMARKS
					Contractor	Third Party	Consultant	
1.0 DOCUMENT REVIEW								
1.1		Material Approval & Shop Drawing - Emergency Vehicle Detection System	QRXP117115-DAH-VORA2R-SPE-INF-R1-Z00000-000001-0B Section 137780 Emergency Vehicle Detection System IFC Drawings QRXP117115-DAH-VORA2R-DWG-ITS-R3-Z00000-2000001 QRXP117115-DAH-VORA2R-DWG-ITS-R3-Z00000-2000002 QRXP117115-DAH-VORA2R-DWG-ITS-R3-Z00000-2000003	QRXM114000-HFC-TEC-MAT-ITS-02-R05-00009 Material Approval Request for EMERGENCY VEHICLE PREEMPTION SYSTEM Approved SHOP DRAWINGS QRXP117115-DAH-VORA2R-DWG-ITS-R3-Z00000-2000001 QRXP117115-DAH-VORA2R-DWG-ITS-R3-Z00000-2000002 QRXP117115-DAH-VORA2R-DWG-ITS-R3-Z00000-2000003	R		H	
1.2		Material Approval & Shop Drawing - Traffic Signal Controller	SHC 306 Section 12.2.3.1 Traffic Signal Controllers IFC Drawings QRXP117115-DAH-VORA2R-DWG-ITS-R3-Z00000-2000001 QRXP117115-DAH-VORA2R-DWG-ITS-R3-Z00000-2000002 QRXP117115-DAH-VORA2R-DWG-ITS-R3-Z00000-2000003	QRXM114000-HFC-TEC-MAT-ITS-02-R05-00007 Material Approval Request for TRAFFIC SIGNAL CONTROLLER Approved SHOP DRAWINGS: QRXP117115-DAH-VORA2R-DWG-ITS-R3-Z00000-2000001 QRXP117115-DAH-VORA2R-DWG-ITS-R3-Z00000-2000002 QRXP117115-DAH-VORA2R-DWG-ITS-R3-Z00000-2000003	R		H	
1.3		Material Approval & Shop Drawing - Transit Signal Priority System	QRXP117115-DAH-VORA2R-SPE-INF-R1-Z00000-000001-0B Section 137750 TRANSIT SIGNAL PRIORITY SYSTEM IFC Drawings QRXP117115-DAH-VORA2R-DWG-ITS-R3-Z00000-2000001 QRXP117115-DAH-VORA2R-DWG-ITS-R3-Z00000-2000002 QRXP117115-DAH-VORA2R-DWG-ITS-R3-Z00000-2000003	QRXM114000-HFC-TEC-MAT-ITS-02-R05-00011 Material Approval Request for TRANSIT SIGNAL PRIORITY SYSTEM Approved SHOP DRAWINGS: QRXP117115-DAH-VORA2R-DWG-ITS-R3-Z00000-2000001 QRXP117115-DAH-VORA2R-DWG-ITS-R3-Z00000-2000002 QRXP117115-DAH-VORA2R-DWG-ITS-R3-Z00000-2000003	R		H	

HAIF-FSA JV Inspection & Test Plan					I &TP		APPROVED DATE	DISCIPLINE
Inteligent Transportation System Works for TRAFFIC SIGNAL SYSTEM					**HFC-ITP-090**			**ITS**
PROJECT TITLE:WBS Access Road To Resort Core (RA2RC)					CONTRACTOR/SUBCONTRACTOR			
WIR No.					CONSTRUCTION- Intelligent Transportation System Works for TRAFFIC SIGNAL SYSTEM		HAIF	

ITEM NO.	PROJECT PHASE	TASK / ACTIVITY	Quality Requirements /references/ specifications	Quality Record	INSPECTION RESPONSIBILITY ASSIGNMENTS			REMARKS
					Contractor	Third Party	Consultant	
1.0 DOCUMENT REVIEW								
1.4		Material Approval & Shop Drawing - Pedestrian Push Button	SHC 306 Section 12.2.3.3 R Pedestrian Push Button IFC Drawings QRXP117115-DAH-VORA2R-DWG-ITS-R3-Z00000-2000001 QRXP117115-DAH-VORA2R-DWG-ITS-R3-Z00000-2000002 QRXP117115-DAH-VORA2R-DWG-ITS-R3-Z00000-2000003	QRXM114000-HFC-TEC-MAT-ITS-02-R05-00013 Material Approval Request for PEDESTRIAN PUSH BUTTON Approved SHOP DRAWINGS: QRXP117115-DAH-VORA2R-DWG-ITS-R3-Z00000-2000001 QRXP117115-DAH-VORA2R-DWG-ITS-R3-Z00000-2000002 QRXP117115-DAH-VORA2R-DWG-ITS-R3-Z00000-2000003	R		H	
1.5		Material Approval & Shop Drawing - Traffic Signal Head	SHC 306 Section 12.2.1.1 Signalization Equipment IFC Drawings QRXP117115-DAH-VORA2R-DWG-ITS-R3-Z00000-2000001 QRXP117115-DAH-VORA2R-DWG-ITS-R3-Z00000-2000002 QRXP117115-DAH-VORA2R-DWG-ITS-R3-Z00000-2000003	QRXM114000-HFC-TEC-MAT-ITS-02-R05-00014 Material Approval Request for TRAFFIC SIGNAL HEAD Approved SHOP DRAWINGS: QRXP117115-DAH-VORA2R-DWG-ITS-R3-Z00000-2000001 QRXP117115-DAH-VORA2R-DWG-ITS-R3-Z00000-2000002 QRXP117115-DAH-VORA2R-DWG-ITS-R3-Z00000-2000003	R		H	
1.6		Material Approval & Shop Drawing- Traffic Signal Poles and Gantries	SHC 306 Section 12.2.2 Supporting Structure Specifications IFC Drawing QRXP117115-DAH-VORA2R-DWG-GEN-R3-Z00000-5000006	QRXM114000-HFC-TEC-MAT-ITS-02-R05-00015 Material Approval Request for TRAFFIC SIGNAL POLES AND GANTRIES Approved SHOP DRAWINGS: QRXM114000-HFC-DRW-SDW-ITS-02-R05-00019-R02 QRXM114000-HFC-DRW-SDW-ITS-02-R05-00031-R01 QRXM114000-HFC-DRW-SDW-ITS-02-R05-00044-R01	R		H	

HAIF-FSA JV Inspection & Test Plan									
Intelligent Transportation System Works for TRAFFIC SIGNAL SYSTEM					I &TP	APPROVED DATE	DISCIPLINE		
PROJECT TITLE/WBS Access Road to Resort Core (RARC)					HFC-ITP-090		ITS		
WIR No.					CONTRACTOR/SUBCONTRACTOR				
					CONSTRUCTION- Intelligent Transportation System Works for TRAFFIC SIGNAL SYSTEM		HAIF		

ITEM NO.	PROJECT PHASE	TASK / ACTIVITY	Quality Requirements /references/ specifications	Quality Record	INSPECTION RESPONSIBILITY ASSIGNMENTS			REMARKS
					Contractor	Third Party	Consultant	
1.0 DOCUMENT REVIEW								
1.7		Material Approval & Shop Drawing - Vehicle Video Detection System	QRXP117115-DAH-VORA2R-SPE-INF-R1-Z00000-000001-0B Section 137714 VEHICLE DETECTION SYSTEM IFC Drawing QRXP117115-DAH-VORA2R-DWG-GEN-R3-Z00000-5000006	QRXM114000-HFC-TEC-MAT-ITS-02-R05-00010 Material Approval Request for VEHICLE VIDEO DETECTION SYSTEM Approved SHOP DRAWINGS: QRXM114000-HFC-DRW-SDW-ITS-02-R05-00019-R02 QRXM114000-HFC-DRW-SDW-ITS-02-R05-00031-R01 QRXM114000-HFC-DRW-SDW-ITS-02-R05-00044-R01	R		H	
2.0 MATERIAL RECEIVING INSPECTION								
2		Material receiving inspection, protection & storage	QD0002-ADM-TEM-QMS00007[0A] MaterialReceiving Inspection in site HFC-CKL-9001	QD0002-ADM-TEM-QMS00007[0A] MaterialReceivingInspection in site HFC-CKL-9001	H		H	MIR to be submitted
3.0 WORK INSTALLATION								
3.1		PRE - INSTALLATION	HFC-CKL-9002	HFC-CKL-9002	H		H	
3.2		INSTALLATION	HFC-CKL-9003	HFC-CKL-9003	H		H	
3.3		TESTING	HFC-CKL-9004	HFC-CKL-9004	H		H	

GENERAL NOTES

1	Surveillance: QA/QC organization to monitor work in progress without notice from Construction Organization
2	Witness: QA/QC organization shall be notified of the timing of inspection or test in advance. However, the inspection or test shall be performed as scheduled if the QA/QC organization representative is not present
3	Hold: QA/QC organization shall be notified of the timing of inspection or test in advance. Inspection or test shall not be carried out without the QA/QC organization representative in attendance.
4	If the Main Contractor delegates the assigned responsibility to the Subcontractor, then the Main Contractor will have the same degree of responsibility as assigned to Consultant.

LEGEND

H	Hold Point for QC Inspection/ Test	R	Review of Documents
W	Witness Inspection/T	RH	Review & approval of Documents
S	Surveillance		

Checklist : HFC-CKL-9001

Material receiving inspection, protection & storage

PROJECT TITLE: Road Access To Resort Core (RA2RC)

WIR No.

Checklist	APPROVED DATE	DISCIPLINE
HFC-CKL-9001		ITS

CONTRACTOR/SUBCONTRACTOR

CONSTRUCTION- Intelligent Transportation System Works for INSTALLATION AND OPERATION of TRAFFIC SIGNAL SYSTEM — HAIF

ITEM NO.	Check Points & Acceptance Criteria	Reference	Pass	Fail	Not Applicable	Re-Inspection
1.0	**Material receiving inspection,protection & storage of TRAFFIC SIGNAL SYSTEM**					
A	Deliver, store, and handle products, using means and methods that will prevent damage, deterioration, and loss, including theft and vandalism. Comply with manufacturer's written instructions.	project specification QRXP117115-DAH-VORA2R-SPE-INF-Z00000-000001-0H 1.7 PRODUCT DELIVERY, STORAGE AND HANDLING	✓			
B	Delivery and Handling:		✓			
1.0	Schedule delivery to minimize long-term storage at Project site and to prevent overcrowding of construction spaces.	project specification QRXP117115-DAH-VORA2R-SPE-INF-Z00000-000001-0H 1.7 PRODUCT DELIVERY, STORAGE AND HANDLING	✓			
2.0	Coordinate delivery with installation time to ensure minimum holding time for items that are flammable, hazardous, easily damaged, or sensitive to deterioration, theft, and other losses.	project specification QRXP117115-DAH-VORA2R-SPE-INF-Z00000-000001-0H 1.7 PRODUCT DELIVERY, STORAGE AND HANDLING	✓			
3.0	Deliver products to Project site in an undamaged condition in manufacturer's original sealed container or other packaging system, complete with labels and instructions for handling, storing, unpacking, protecting, and installing.	project specification QRXP117115-DAH-VORA2R-SPE-INF-Z00000-000001-0H 1.7 PRODUCT DELIVERY, STORAGE AND HANDLING	✓			
4.0	Inspect products on delivery to determine compliance with the Contract Documents and that products are undamaged and properly protected.	project specification QRXP117115-DAH-VORA2R-SPE-INF-Z00000-000001-0H 1.7 PRODUCT DELIVERY, STORAGE AND HANDLING	✓			
C	Storage:					
1.0	Provide a secure location and enclosure at Project site for storage of materials and equipment.	project specification QRXP117115-DAH-VORA2R-SPE-INF-Z00000-000001-0H 1.7 PRODUCT DELIVERY, STORAGE AND HANDLING	✓			
2.0	Store products to allow for inspection and measurement of quantity or counting of units.	project specification QRXP117115-DAH-VORA2R-SPE-INF-Z00000-000001-0H 1.7 PRODUCT DELIVERY, STORAGE AND HANDLING	✓			
3.0	Store materials in a manner that will not endanger Project structure.	project specification QRXP117115-DAH-VORA2R-SPE-INF-Z00000-000001-0H 1.7 PRODUCT DELIVERY, STORAGE AND HANDLING	✓			
4.0	Store products that are subject to damage by the elements under cover in a weathertight enclosure above ground, with ventilation adequate to prevent condensation and with adequate protection from wind.	project specification QRXP117115-DAH-VORA2R-SPE-INF-Z00000-000001-0H 1.7 PRODUCT DELIVERY, STORAGE AND HANDLING	✓			
5.0	Protect foam plastic from exposure to sunlight, except to extent necessary for period of installation and concealment.	project specification QRXP117115-DAH-VORA2R-SPE-INF-Z00000-000001-0H 1.7 PRODUCT DELIVERY, STORAGE AND HANDLING	✓			
6.0	Comply with product manufacturer's written instructions for temperature, humidity, ventilation, and weather-protection requirements for storage.	project specification QRXP117115-DAH-VORA2R-SPE-INF-Z00000-000001-0H 1.7 PRODUCT DELIVERY, STORAGE AND HANDLING	–			
7.0	Protect stored products from damage and liquids from freezing.	project specification QRXP117115-DAH-VORA2R-SPE-INF-Z00000-000001-0H 1.7 PRODUCT DELIVERY, STORAGE AND HANDLING	✓			
8.0	Provide a secure location and enclosure at Project site for storage of materials and equipment by Employer's construction forces. Coordinate location with Employer.	project specification QRXP117115-DAH-VORA2R-SPE-INF-Z00000-000001-0H 1.7 PRODUCT DELIVERY, STORAGE AND HANDLING	✓			

Remarks

PM/Contractor

Contractor Construction

The work is ready for inspection

Name	Signature	Date
Mahmoud		11/7/26
Contractor QC Inspector		
MRAMMuhammad		09/07/026

QDC

Third Party (if applicable)

Document Reviewed	Work Inspected	Test Records Verified

Name	Signature
QDC Supervision Consultant	
A. Hassan Ibrahim	

Form Ref.No. QD0002-ADM-TEM-QTY-00003-Rev.00

TRAFFIC TECH
www.traffic-tech.com

تقنيات المرور الأمنية ذ.م.م.
TRAFFIC TECH SECURITY W.L.L.

Date: 06-july-2026
Our Ref: TTSDN-Haif-060726-026

Delivery Note

To: HAIF COMPANY

الى:

Ref: WS045CR-53 (RA2RC – ACCESS ROAD TO RESORT CORE)

SN	Model No. رقم الموديل	Description الوصـــــف	Unit الوحـدة	Qty الكميـة	Remarks ملاحظـات
MATERIAL SUPPLY (TRAFFIC SIGNALS)					
1		3.7 M TRAFFIC SIGNAL POLE	NOS	39	

Delivered By: EHAB BASLA

Printed Name & Signature

Date: 06-07-2026

Received By:

Printed Name & Signature

Date: 6-7-2026

شركة هائل للمقاولات
Haif Contracting
Date
Project. Qiddiya
WS-045CR
Received

شركة تقنيات المرور الأمنية ذ.م.م.
TRAFFIC TECH
سجل تجاري
١٠١٠٨٨٢٧٣٢
TRAFFIC TECH Security W.L.L. Co.

Unit No. 38, Building 3990
Anas Bin Malik St., Al Malga District
P.O. Box 13524
6615, Riyadh, Saudi Arabia
E-mail : ttg@traffic-tech.com
Web: www.traffic-tech.com

شركة عميقة للفوانيس والأعمدة والجلفنة
OMEGA COMPANY FOR LUMINAIRES, POLES & GALVANIZING

DELIVERY NOTE مذكرة تسليم

No.:	WH1/OUT/02941	الرقم	Date:	05/07/2026	التاريخ	Job No.:	JP-000863	رقم التشغيل

To: إلى

Traffic Tech Security W.L.L.
Al Olaya , 1
Riyadh (SA), Riyadh
Saudi Arabia

Delivery At: C & F

Contact Person Mr. Talha Tufail Abbasi :الشخص المسئول

Customer P.O. No. POR-2026-0022 :رقم أمر شراء العميل

M.R. No فسح رقم:

بند Item	الرمز Code	البيان Description	الوحدة UNIT	الكمية Qty.	الوزن Gross Wt.
1	S-9571-R2	3.7 M TUBULAR TRAFFIC SIGNAL POLE W/ TOP BOLTED CAP & BASE PLATE ONLY. DWG. NO. S-9571. REV. 02.	Nos	39.0	
2	TRS-1	TRANSPORTATION CHARGES.	Nos	1.0	

Prepared by: أعد بواسطة | Approved by: اعتمدت بواسطة

Carrier Name: OMEGA FAISAL إسم الشركة الناقلة

Vehicle Plate No.: 7421 VTA رقم اللوحة :

Driver's Name: MAZAR IQBAL اسم السائق

Driver's Sign.: توقيع السائق Date.: 05/07/26 التاريخ

DOC 17 : REV 1 : DCR/A 055 : 25/08/2020

تشهد أن البضاعة أستلمت بحالة جيدة.
Hereby Confirm Above Goods Received in Good Condition

اسم الشخص المسئول وتوقيعه
Customer's Authorized Person's

Name EHAB Rafiq اسم

Sign : EHAB التوقيع

0559787860

06-07-2026

C.R. 1010060362, COC Membership 91310
P.O. Box 22258, Riyadh 11495, Saudi Arabia
Tel.: +966 11 498 4587, Fax: +966 11 498 2383
E-Mail : omega@omega-abahsain.com

Website: omega-abahsain.com

سجل تجاري ١٠١٠٠٦٠٣٦٢ - رقم العضوية ٩١٣١٠
ص.ب ٢٢٢٥٨ الرياض ١١٤٩٥ - المملكة العربية السعودية
تلفون: ٤٥٨٧ ٤٩٨ ١١ ٩٦٦+ - فاكس: ٢٣٨٣ ٤٩٨ ١١ ٩٦٦+
بريد الكتروني : omega@omega-abahsain.com

شركـــــة عميقـــــة للفوانيس والأعمـــدة والجلفنـــة
OMEGA COMPANY FOR LUMINAIRES, POLES & GALVANIZING

DELIVERY NOTE مذكرة تسليم

No.: WH1/OUT/02942 الرقم	Date: 05/07/2026 التاريخ	Job No.: JP-000954 رقم التشغيل

To: إلى
Traffic Tech Security W.L.L.
Al Olaya , 1
Riyadh (SA), Riyadh
Saudi Arabia
Delivery At: C & F

Contact Person Mr. Talha Tufail Abbasi الشخص المسئول:
Customer P.O. No. POR-2026-0025 رقم أمر شراء العميل:
M.R. No فسح رقم:

بند Item	الرمز Code	البيان Description	الوحدة UNIT	الكمية Qty.	الوزن Gross Wt.
1	PC-2	POWDER COATING CHARGES FOR THE 3.7 M POLE (JP-000863), COLOR RAL - 7015 (M) MATT FINISH.	Nos	39.0	

Prepared by: أعد بواسطة
Approved by: اعتمدت بواسطة

Carrier Name: OMEGA / FAHAD إسم الشركة الناقلة
Vehicle Plate No.: 7421 YTA رقم اللوحة :
Driver's Name: MAZAR IQBAL اسم السائق
Driver's Sign.: توقيع السائق Date.: التاريخ 05/07/26

DOC 17 : REV 1 : DCR/A 055 : 25/08/2020

تشهد أن البضاعة أستلمت بحالة جيدة.
Hereby Confirm Above Goods Received in Good Condition

اسم الشخص المسئول وتوقيعه
Customer's Authorized Person's

Name EHAB Basha اسم:
Sign : EHAB التوقيع

0591787880

06-07-2026

C.R. 1010060362, COC Membership 91310
P.O. Box 22258, Riyadh 11495, Saudi Arabia
Tel.: +966 11 498 4587, Fax: +966 11 498 2383
E-Mail : omega@omega-abahsain.com

Website: omega-abahsain.com

سجل تجاري ١٠١٠٠٦٠٣٦٢ - رقم العضوية ٩١٣١٠
ص.ب ٢٢٢٥٨ الرياض ١١٤٩٥ - المملكة العربية السعودية
تلفون: ٤٥٨٧ ٤٩٨ ١١ ٩٦٦+ - فاكس: ٢٣٨٣ ٤٩٨ ١١ ٩٦٦+
بريد الكتروني : omega@omega-abahsain.com

شركـــــة عميقـــــــة للفوانيس والأعمـــدة والجلفنـــة
OMEGA COMPANY FOR LUMINAIRES, POLES & GALVANIZING

Quality Control Department

Date : **July 7, 2026**

Our reference : **JP - 000863**

Your reference : **P.O. No. POR-2026-0022 Dated 13-04-2026**

Certificate No. : **2641**

Customer : **M/S Traffic Tech Security W.L.L**

GALVANIZATION CERTIFICATE

We hereby certify that the Steel Articles mentioned below have been hot dip galvanized in accordance with **ASTM A123** Specification.

MATERIALS INSPECTED:

SR #	DESCRIPTIONS	UNIT	QUANTITY
1.0	3.7 M TUBULAR TRAFFIC SIGNAL POLE W/ TOP BOLTED CAP & BASE PLATE ONLY, DWG. NO. S-9571 REV. 02.	EACH	39

For
O M E G A C O M P A N Y
Div. of S & A Abahsain Co. Ltd.

SHAIK ARSHAD
QA/QC in Charge

OMEGA COMPANY
PASSED
INSP.
QUALITY CONTROL

QUALITY CONTROL REPORT

Date : 06/07/2026

UNICOAT
الطلاء الفريد

شركة الطلاء الفريد المحدودة
Unique Coating Co.Ltd

CUSTOMER: OMEGA COMPANY

RAL NO : 7015 MATTE POWDER BATCH NO: 25072401

DATE OF DELIVERY: ---------- DELIVERY NO :

PROJECT NAME: PROJECT CODE:

MATERIAL TYPE : GALVANIZED STEEL POLE DELIVERY #:

TOTAL QUANTITY: 39 PIECE

TOTAL WEIGHT -- -- KGS---- TOTAL SQM: 0.000

VISUAL APPEARANCE	REQUIREMENTS	RESULTS	REMARKS
COATING THICKNESS AAMA/ 2603 / 2604	GALVANIZED READING & TOP COAT 8019 HR	Min. 148 um Max. 175 um Ave. 160 um	SINGLE COAT PASSED
GLOSS / AAMA / 2603 / 2604	20 + - 5 GU	Min. 18 GU Max. 19 GU Ave. 20 GU	PASSED


PRODUCT/SAMPLE MECHANICAL TEST		
PERFORMANCE TEST	METHOD OF INSPECTION	OBSERVATION
IMPACT TEST ASTM D 2794	KGS/CM	PASSED
ADHESION TEST ASTM D 3359	CROSS HATCH	PASSED
FLEXIBILITY BENDING TEST ASTM D 522	CONICAL MANDREL BEND	PASSED
CURING TEST ASTM D 4752	METHYL ETHYL KETONE	PASSED

CHEMICAL CONCENTRATION	REQUIREMENTS	RESULTS	REMARKS
VALOPHOS 044S	Maintained to 1-5 % CON	5.63 % v/v	PASSED
VALOPHOS F87, VALOADD IP	Consumed NAOH	8.75 % v/v	PASSED
WATER RINSING	Conductivity below 30 us	16.5 us	PASSED

شركة الطلاء الفريد المحدودة
Unique Coating Co. Ltd.


CUSTOMER SIGNATURE:

I RECEIVED THE MATERIAL COMPLETE AND GOOD CONDITION

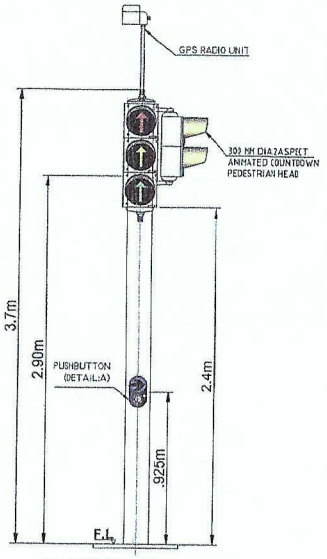


3.7m TYPICAL GPS RADIO UNIT INSTALLATION

SCALE: N.T.S.

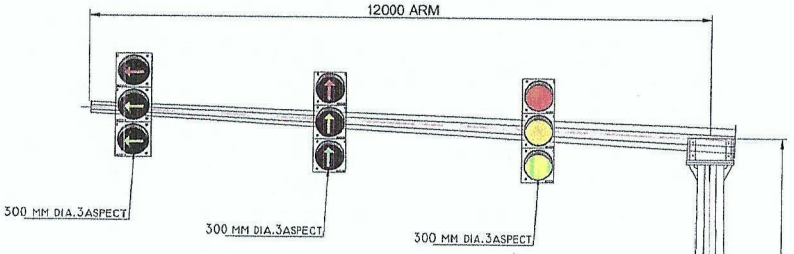


TYPICAL SIGNAL GANTRY (CANTILEVER) DETAIL GANTRY NO - 10

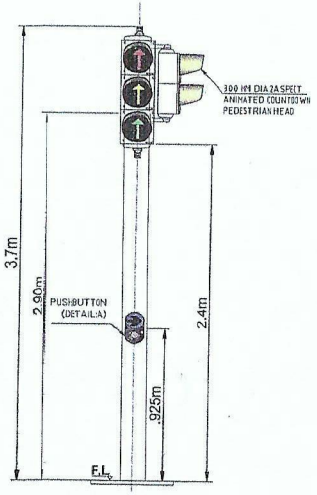


3.7m TRAFFIC SIGNAL HEADS, PED HEADS & PUSHBUTTON MOUNTING TYPICAL DETAILS

SCALE: N.T.S.

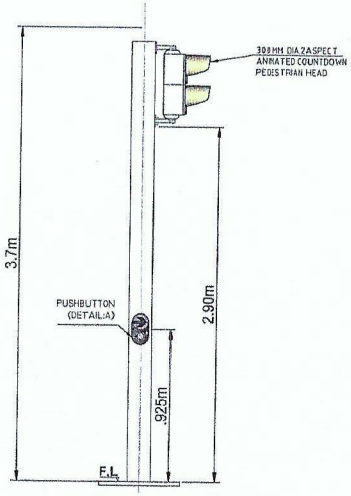


3.7m PED HEADS & PUSHBUTTON MOUNTING TYPICAL DETAILS

SCALE: N.T.S.

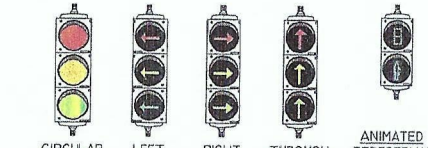


TYPICAL VEHICULAR / PEDESTRIAN SIGNAL HEAD DETAILS

SCALE: N.T.S.

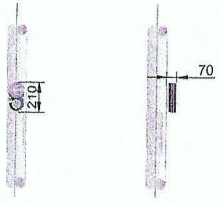

DETAIL-A: PUSH BUTTON

SCALE: N.T.S.

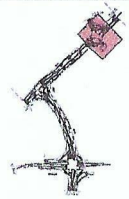

Notes:
1. ALL DIMENSIONS ARE IN MILLIMETER UNLESS OTHERWISE STATED.
2. ALL LEVELS ARE IN METERS UNLESS NOTED OTHERWISE.
3. THIS DRAWINGS IS TO BE READ IN CONJUNCTION WITH ALL RELEVANT ARCHITECTURAL, STRUCTURAL AND SERVICES DRAWINGS.

REFERENCE I.F.C DESIGN DRAWING NO:
1. QRXP17115-DAR-VDRA2R-DWG-ITS-R3-Z00000-1000001
2. QRXP17115-DAR-VDRA2R-DWG-ITS-R3-Z00000-5000001
3. QRXP17115-DAR-VDRA2R-DWG-ITS-R3-Z00000-5000002
4. QRXP17115-DAR-VDRA2R-DWG-ITS-R3-Z00000-5000005
5. QRXP17115-DAR-VDRA2R-DWG-ITS-R3-Z00000-5000006
6. QRXP17115-DAR-VDRA2R-DWG-ITS-R3-Z00000-6000001
7. QRXP17115-DAR-VDRA2R-DWG-ITS-R3-Z00000-6000002
8. QRXP17115-DAR-VDRA2R-DWG-ICT-R3-Z00000-2000009

LEGEND:

Rev. No.	Date	Description	Appr.
00	31-8-2025	FOR REVIEW AND APPROVAL	C
01	08-11-2025	FOR REVIEW AND APPROVAL	C
02	26-12-2025	FOR REVIEW AND APPROVAL	--
--	--	--	--
--	--	--	--
--	--	--	--
--	--	--	--

Consultant

Contractor

ITS Contractor

Project:

Job title: Road Access To Resort Core

Drawing title:
SHOPDRAWING OF TRAFFIC SIGNAL SYSTEM FOR JUNCTION-3
TYPICAL DETAILS-2+GPS RADIO UNIT ON 3.7m TRAFFIC SIGNAL POLE

Sheet number:
SHEET 6 / 20

Scale:NTS

Drawn:M.Sayed	Checked:M.Sayed
Designed:	Approved:


Drawing number: QRXM114000-HFC-DRW-SDW-ITS-02-R05-D0038

Revision 02

Consultant's information
HEAD OFFICE - Riyadh
6283 King Abdul Aziz Rd, Ar Rabi
Riyadh 13316 2771, Saudi Arabia
Tel.: +966 11 4048484
Fax : +966 11 4048400
Website : www.zfp.com
Email.: zfpr@zfp.com

Noted :

1. ITS Cabinet location is already beeton site and coordinated with the traffic signal controller as per approved shop drawings.
2. The junction box LPR is suitable for outdoor application

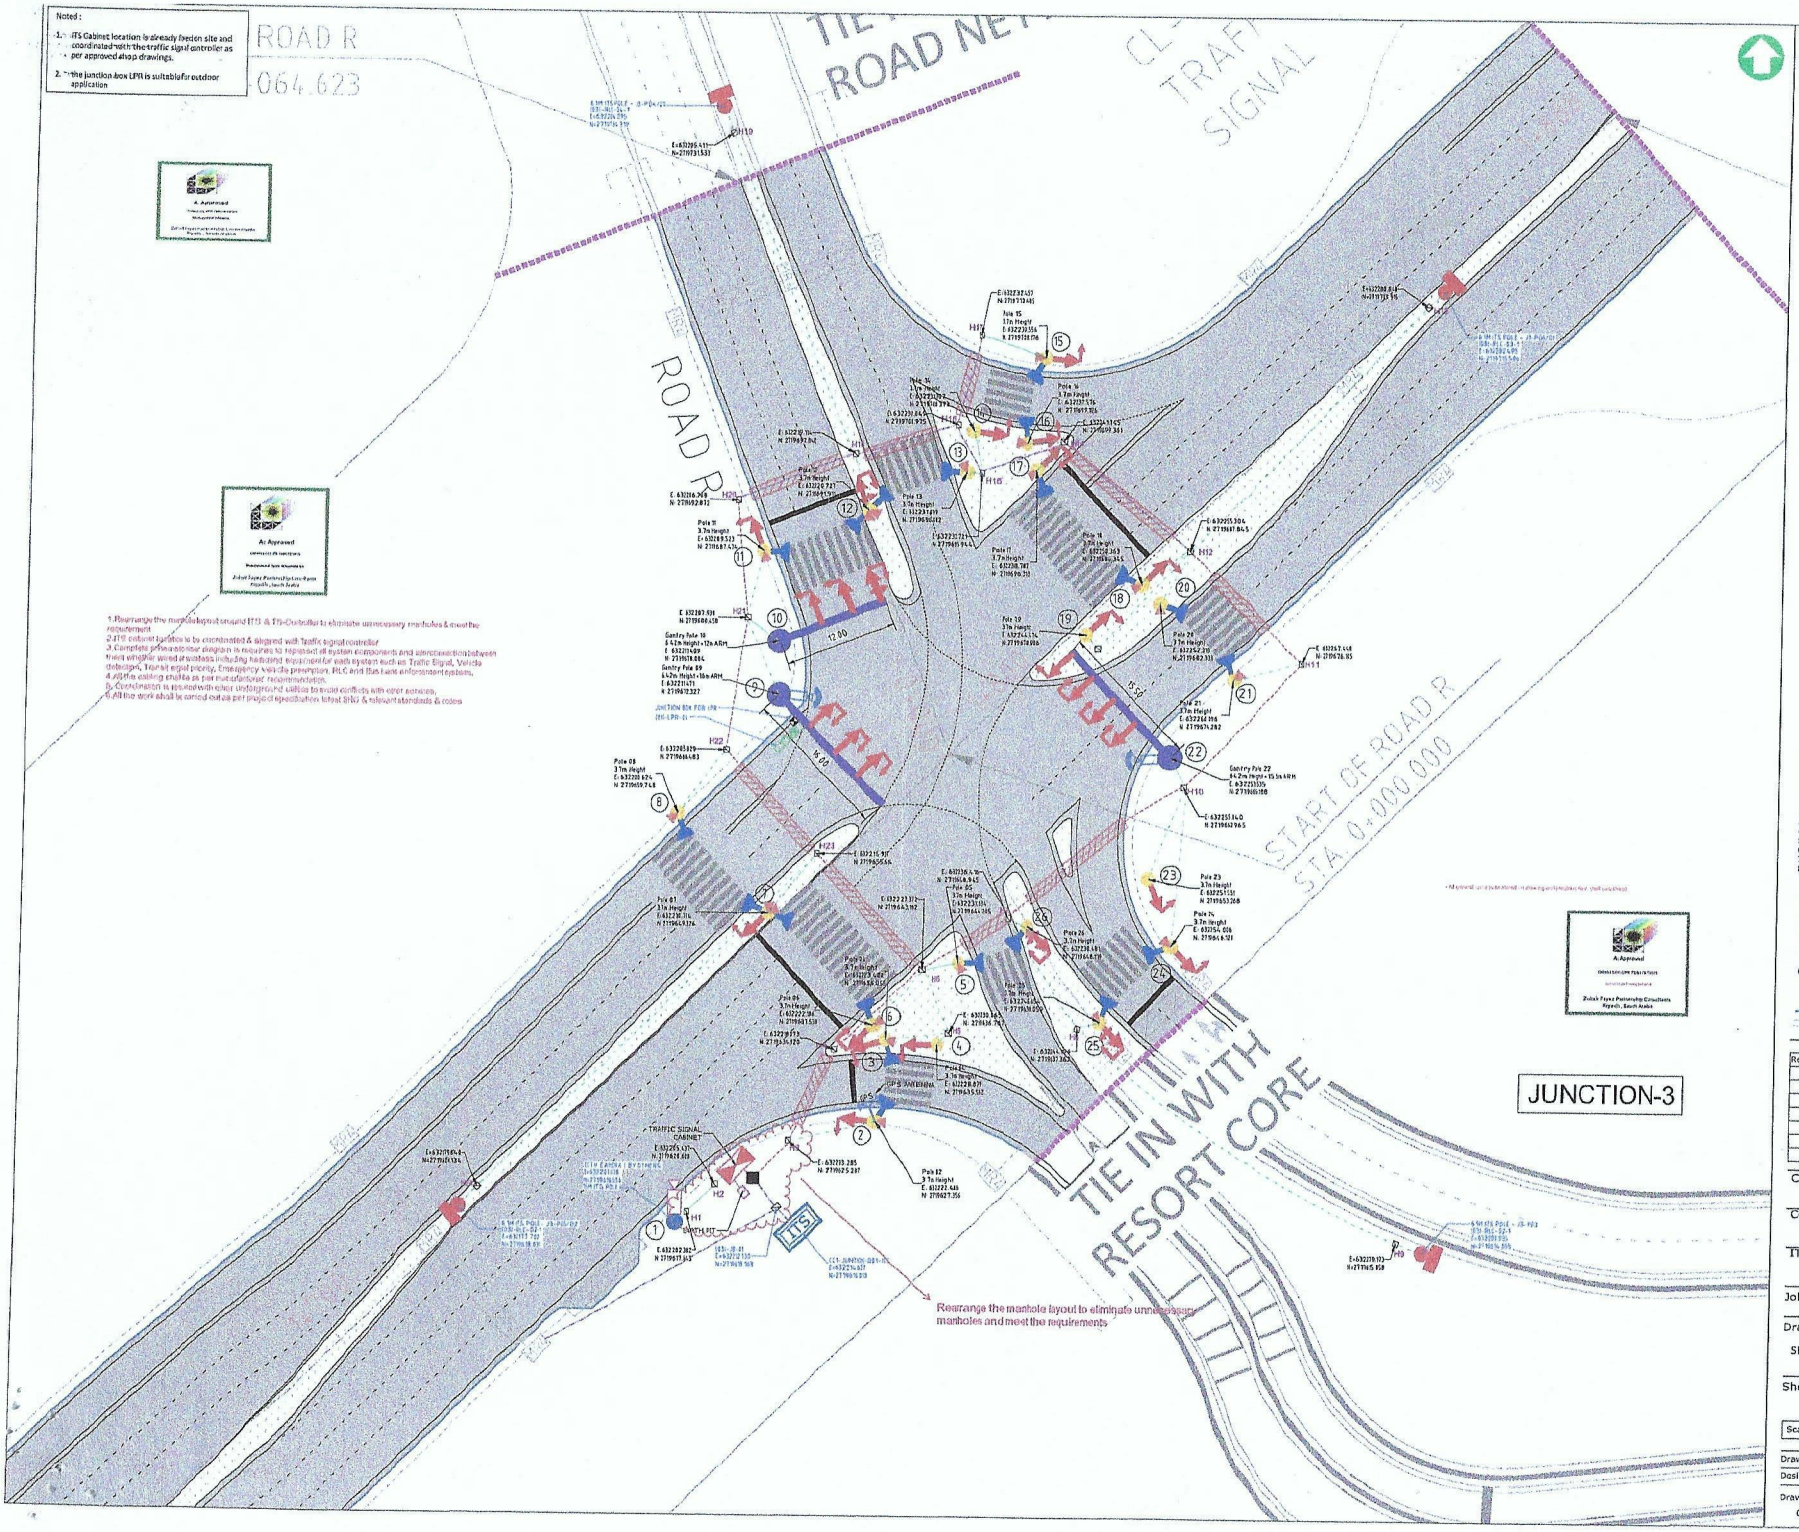


القديـــة
Qiddiya

Consultant's information

HEAD OFFICE - Riyadh
6283 King Abdul AzizRd, Ar Rabi
Riyadh 13316 2771, Saudi Arabia
Tel.: +966 11 4048484
Fax : +966 11 4048490
Website : www.zfp.com
Email.: zfpr@zfp.com


Zuhair Fayez Partnership

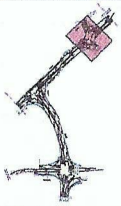

Notes:
1. ALL DIMENSIONS ARE IN MILLIMETER UNLESS OTHERWISE STATED.
2. ALL LEVELS ARE IN METERS UNLESS NOTED OTHERWISE.
3. THIS DRAWINGS IS TO BE READ IN CONJUNCTION WITH ALL RELEVANT ARCHITECTURAL, STRUCTURAL AND SERVICES DRAWINGS.

REFERENCE I.F.C DESIGN DRAWING NO:
1. QRXP117115-DAH-VORA2R-DWG-ITS-R3-200000-2000003
2. QRXP117115-DAH-VORA2R-DWG-ITS-R3-200000-5000001
3. QRXP117115-DAH-VORA2R-DWG-ITS-R3-200000-5000002
4. QRXP117115-DAH-VORA2R-DWG-ITS-R3-200000-5000005
5. QRXP117115-DAH-VORA2R-DWG-ITS-R3-200000-5000006
6. QRXP117115-DAH-VORA2R-DWG-ITS-R3-200000-6000001
7. QRXP117115-DAH-VORA2R-DWG-ITS-R3-200000-6000002
8. QRXP117115-DAH-VORA2R-DWG-ICT-R3-200000-2000000

LEGEND:

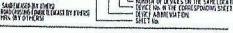

Rev. No.	Date	Description	Appr.
00	31-8-2025	FOR REVIEW AND APPROVAL	C
01	08-11-2025	FOR REVIEW AND APPROVAL	B
02	04-02-2026	FINAL REVISION	-
--	--	--	--
--	--	--	--
--	--	--	--
--	--	--	--

Consultant

Contractor
شركة مرفق
Hall Company

ITS Contractor
TRAFFIC

Project:
القديـــة
Qiddiya

Job title: Road Access To Resort Core

Drawing title: SHOPDRAWING OF TRAFFIC SIGNAL SYSTEM FOR JUNCTION-3

Sheet number: SHEET 1 / 20

Scale:1:1000 @ A0

Drawn: M.Elsayed | Checked: M.Abuzaid
Designed: | Approved:

Drawing number: QRXM114000-HFC-DRW-SDW-ITS-02-R05-D0033 | Revision 02

